PELAN
MPBP.Blg
37.2

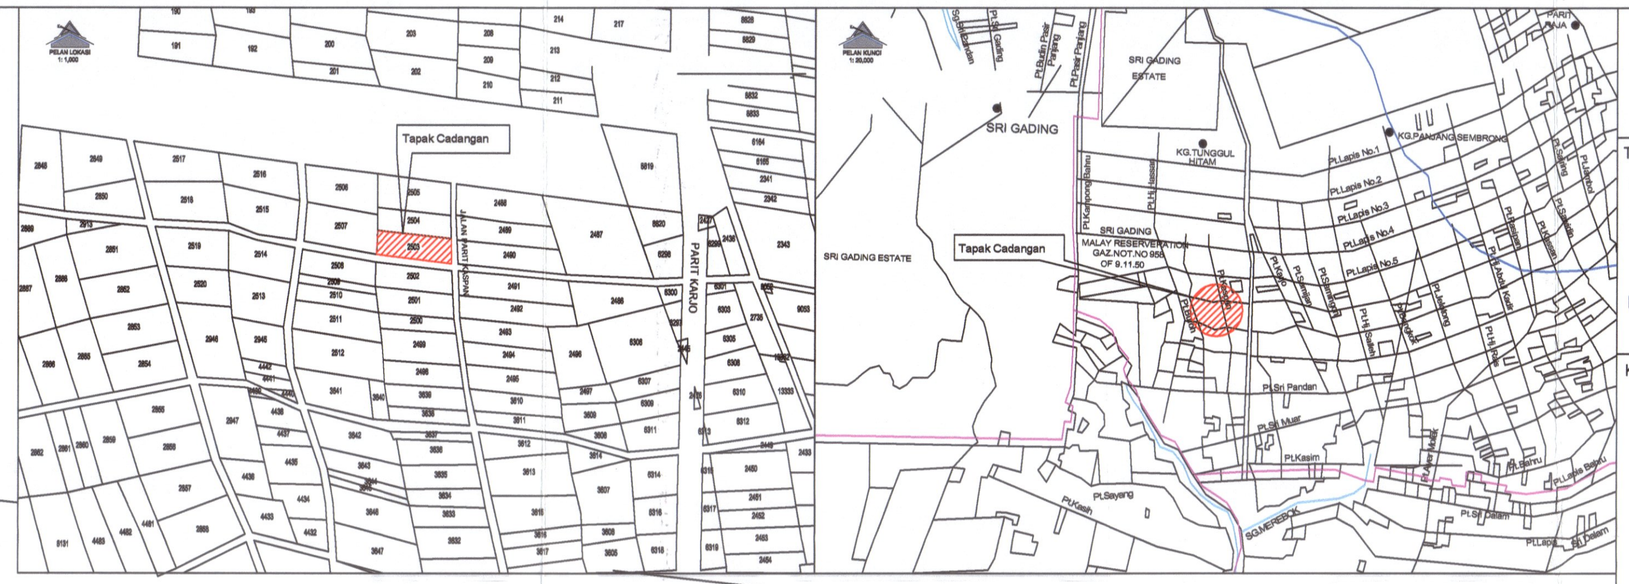

SKALA 1: 400
SYIT PIAWAI : 49 B III

TAJUK PELAN :

PELAN PRA-HITUNGAN UNTUK PERMOHONAN KEBENARAN MERANCANG SUSUNAN PENGGUNAAN TANAH UNTUK PECAH SEMPADAN YANG MELIBATKAN PENDIRIAN BANGUNAN MENGIKUT SEKSYEN 21, AKTA PERANCANGAN BANDAR DAN DESA 1976 (AKTA 172) , BAGI TUJUAN PEMBANGUNAN 20 UNIT RUMAH SESEBUAH DI ATAS LOT 2503, GM 10926, SELUAS 1.2318 HEKTAR,MUKIM SRI GADING DAERAH BATU PAHAT, JOHOR DARUL TAKZIM

KEGUNAAN MPBP

No. Fail	MPBP-BM78/2021-04/25
No. Pelan Susun Atur	B4.1
No. LCP	37.3
No. Pelan Pra-Hitungan	37.2

Pelan Pra-Hitungan ini telah disemak dan diakui menepati Pelan Susun Atur. Pelan ini handakan dibaca bersama-sama Pelan Susun Atur, Laporan Cadangan Pemajuan (LCP) dan syarat-syarat pemajuan pada lampiran di Borang C(1) bertarikh 31 JUL 2021

Disemak:
Shahril bin Karjoo
Ketua Jabatan
Jabatan Perancangan Pembangunan
Majlis Perbandaran Batu Pahat
Tarikh : 31 JUL 2021

Disahkan:
Haji Kamalludin bin Haji Jamal
Yang Dipertua
Majlis Perbandaran Batu Pahat
Tarikh : 31 JUL 2021

KEGUNAAN PTG

Bil. Fail PTG 01/08/03/0100/0080/2022/1012/2022
Disemak mengikut / ~~tidak mengikut~~
Pelan MPBP. BLG (371)
Bgm. ~~JHIB(T)~~ Rm 143/2023
Bertarikh 18/11/2023
Oleh,

DISAHKAN OLEH,

"MUHAMMAD IZZAT BIN KAMDAR"
Pendaftar Pejabat Tanah (N29)
Pejabat Tanah Dan Galian Johor

"NORLIYATI BINTI MD NOR"
Timbalan Pengarah (Pembangunan)
Pejabat Tanah Dan Galian Johor

JADUAL PETUNJUK :

JENIS KEGUNAAN TANAH	UNIT	LUAS(mp)	LUAS(ek)	% LUAS
Rumah Sesebuah	20	8116mp	2.005ek	65.89
Ritab Jalan		2322mp	0.574ek	18.85
Ritab Parit		872mp	0.215ek	7.07
Kawasan Lapang		983mp	0.243ek	7.98
TNB (Compact Sub)	1	25mp	0.006ek	0.20
JUMLAH	21	12318mp	3.043ek	100

NOTA :
KELUASAN, BERING DAN JARAK MUNGKIN BERUBAH SETELAH UKURAN MUKTAMAD DUALANKAN

TANDATANGAN PEMILIK / PEMOHON :

SHAHRULANUAR BIN ZAINAL ARIFFIN
690204-01-6081
NO.55, TAMAN MAS 1,
43200 BATU 9,
CHERAS, SELANGOR

ZAINAL ARIFFIN BIN AHMAD
390625-01-5015
NO.55, TAMAN MAS 1,
43200 BATU 9,
CHERAS, SELANGOR

JURUUKUR BERTAULIAH :

JURUKUR MAYA
No 1079 Jalan Jambu Batu 3
Taman Muhibbah Saleng
81400, Senai, Johor
Tel :07-7714667 Fax 07-7765514
Tel :019-7186053

Sr. Hj. Mohd Shah Bin Hj. Seeron
(JURUKUR TANAH YANG DILESEN PER 2011
DI BAWAH AKTA 458 (SEMAK 2011))

DI SEMAK OLEH : LIZA 24/08/2021
DI LUKIS OLEH : MAI

PELAN NO : JMY/2021/1499-PRE-COMP

2506
PA 13166

2505

2504
PA 13166

2507
PA 13166

2488

2489
PA 7134

2490
PA 7134

2491
PA 7134

2502
PA 13166

RIZAB JALAN

SIMPANAN JALAN

JALAN PARIT KASPAN

PTD. 26358 PLOT 1 461mp
PTD. 26359 PLOT 2 386mp
PTD. 26360 PLOT 3 386mp
PTD. 26361 PLOT 4 386mp
PTD. 26362 PLOT 5 386mp
PTD. 26363 PLOT 6 386mp
PTD. 26364 PLOT 7 386mp
PTD. 26365 PLOT 8 386mp
PTD. 26366 PLOT 9 386mp
PTD. 26367 PLOT 10 386mp
PTD. 26368 PLOT 11 442mp
PTD. 26369 PLOT 12 402mp
PTD. 26370 PLOT 13 405mp
PTD. 26371 PLOT 14 410mp
PTD. 26372 PLOT 15 412mp
PTD. 26373 PLOT 16 415mp
PTD. 26374 PLOT 17 420mp
PTD. 26375 PLOT 18 422mp
PTD. 26376 PLOT 19 425mp
PTD. 26377 PLOT 20 428mp
PTD. 26378 Kawasan Lapang 983mp
PTD. 26379 TNB (Compact Sub)

2503
1.2318 ha

Rizab parit JPS

194.802
12.192m [40']
19.635m [64']
15.411m [51']
64.720
61.692
18.260
16.957
19.563
11.929
7.035
13.961
27.587
7.848
5.829
13.982
3.048
6.434
0.611
4.000
5.906